
SHOP DRAWING

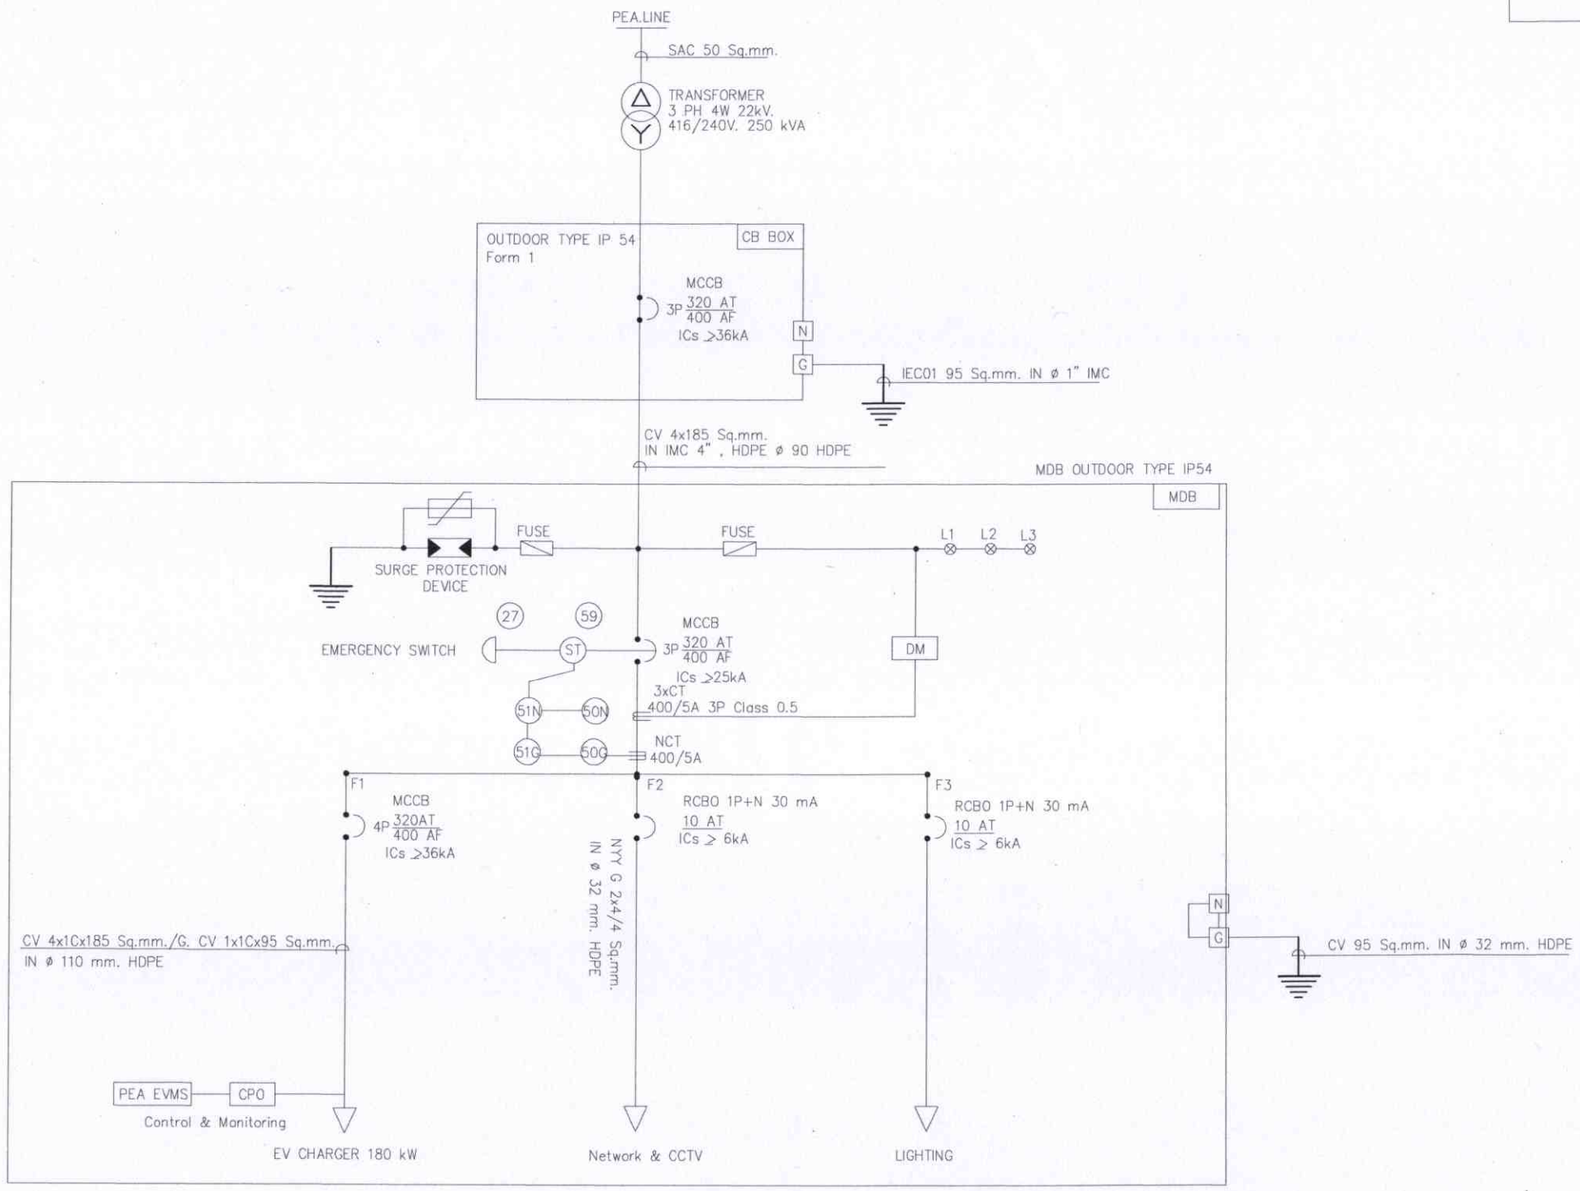

การไฟฟ้าส่วนภูมิภาค

ผู้สำรวจ		โครงการจ้างก่อสร้างพร้อมติดตั้งสถานีอัดประจุไฟฟ้า สำหรับยานยนต์ไฟฟ้า	เขียนเสร็จวันที่ : –
ผู้เขียน			แก้แบบวันที่ : –
วิศวกรไฟฟ้า		สถานที่ : เลขที่ 110 ม. 3 ต.บ้านพร้าว อ.นครไทย จ.พิษณุโลก	มิติ เป็น : –
หัวหน้าแผนก			แบบเลขที่ : PL24-0A3-69015
ผู้อำนวยการกอง		SINGLE LINE DIAGRAM	แผ่นที่ 3 ของจำนวน 16 แผ่น
ผู้อำนวยการฝ่าย			

ELECTRICAL CERTIFICATION	
SIGNATURE	
NAME	
LICENCE NO.	